




附件八：工艺流程控制图

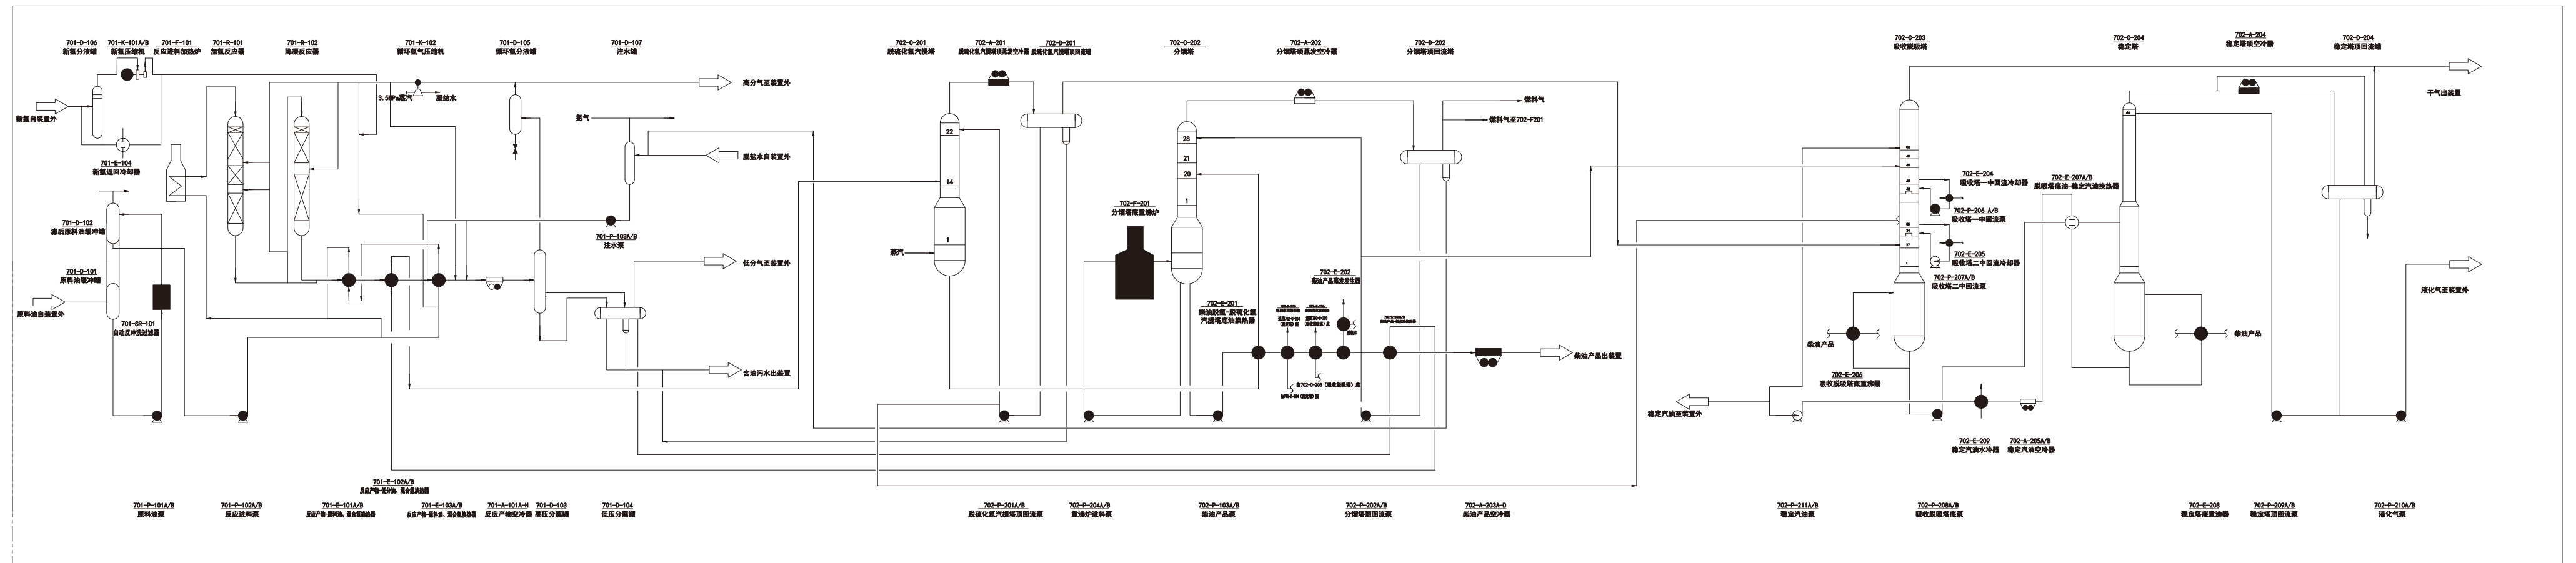


附件九：设备平面布置图

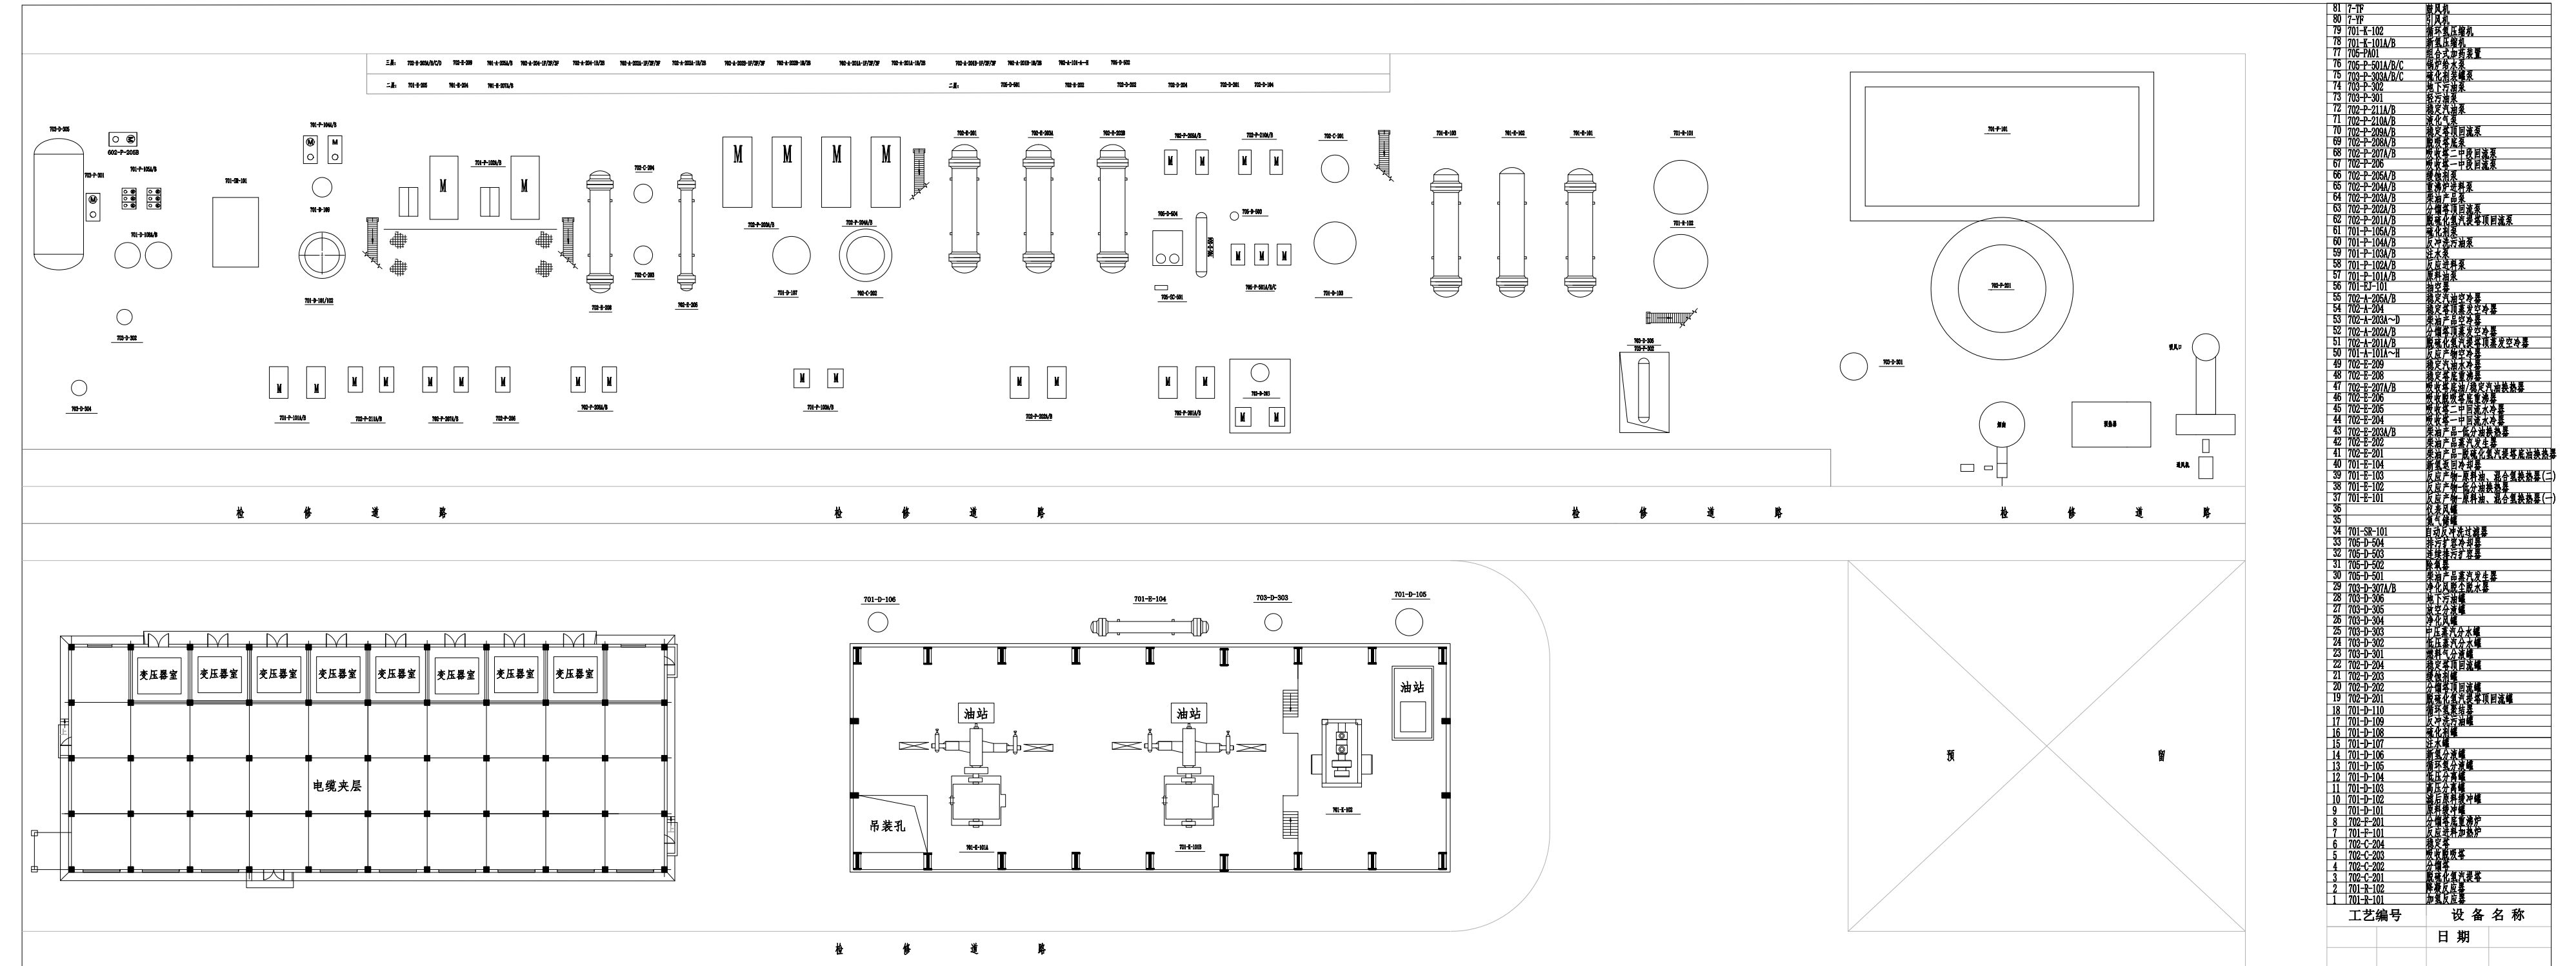

附件十：设备竖面布置图

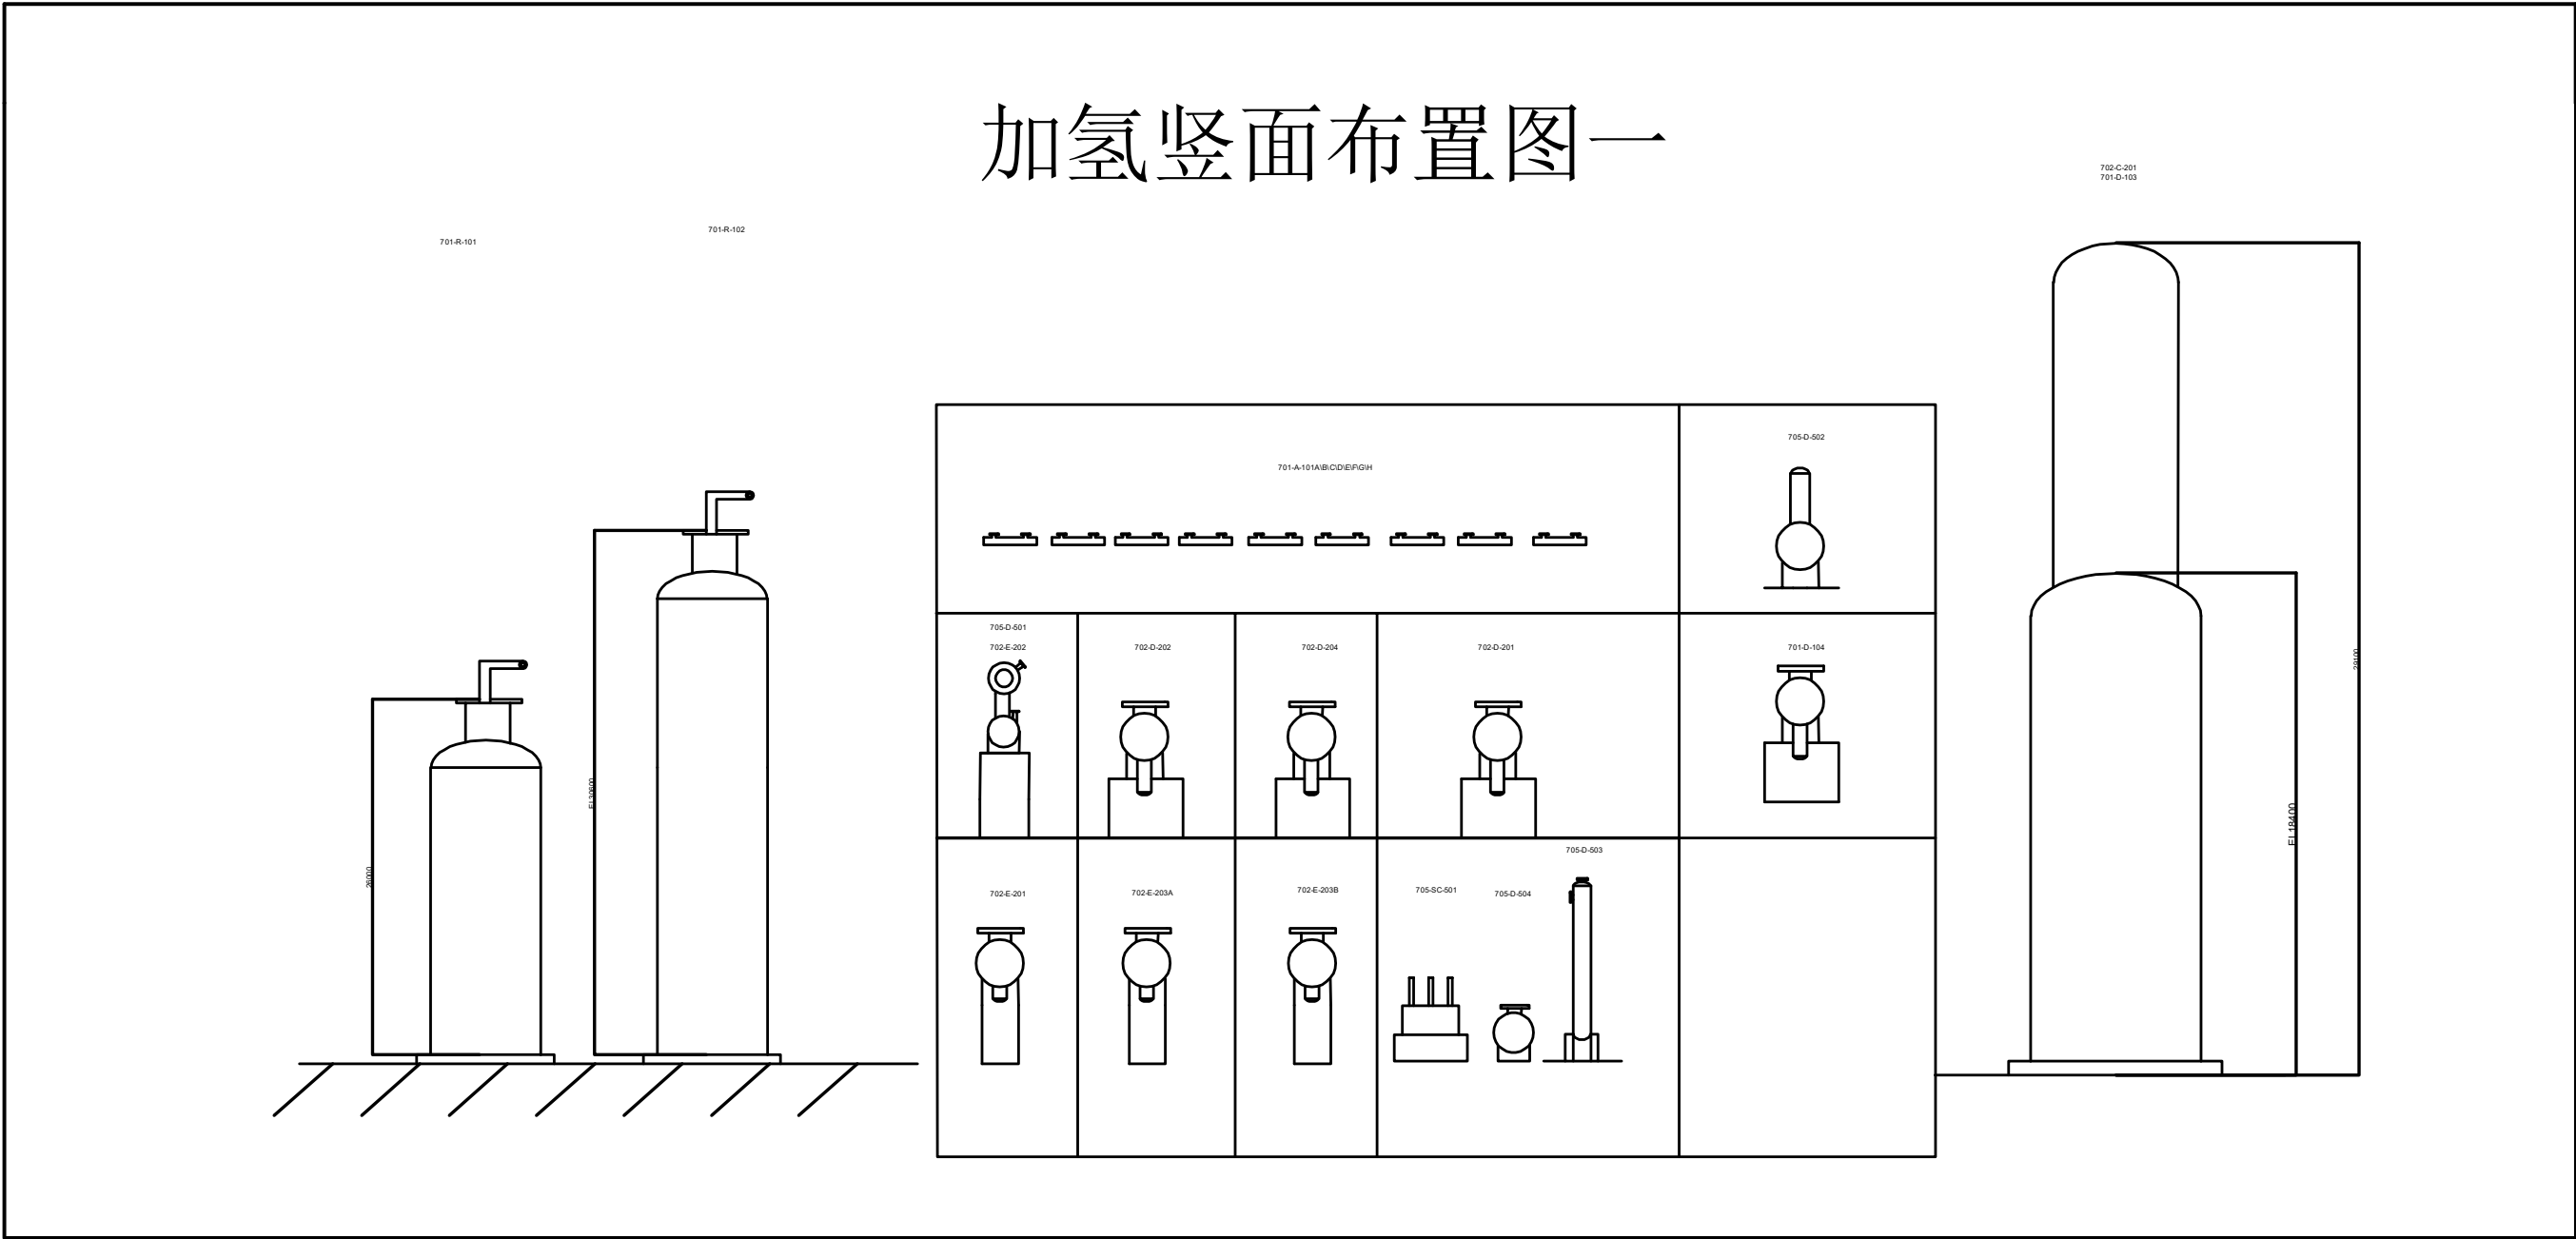

加氢竖面布置图二

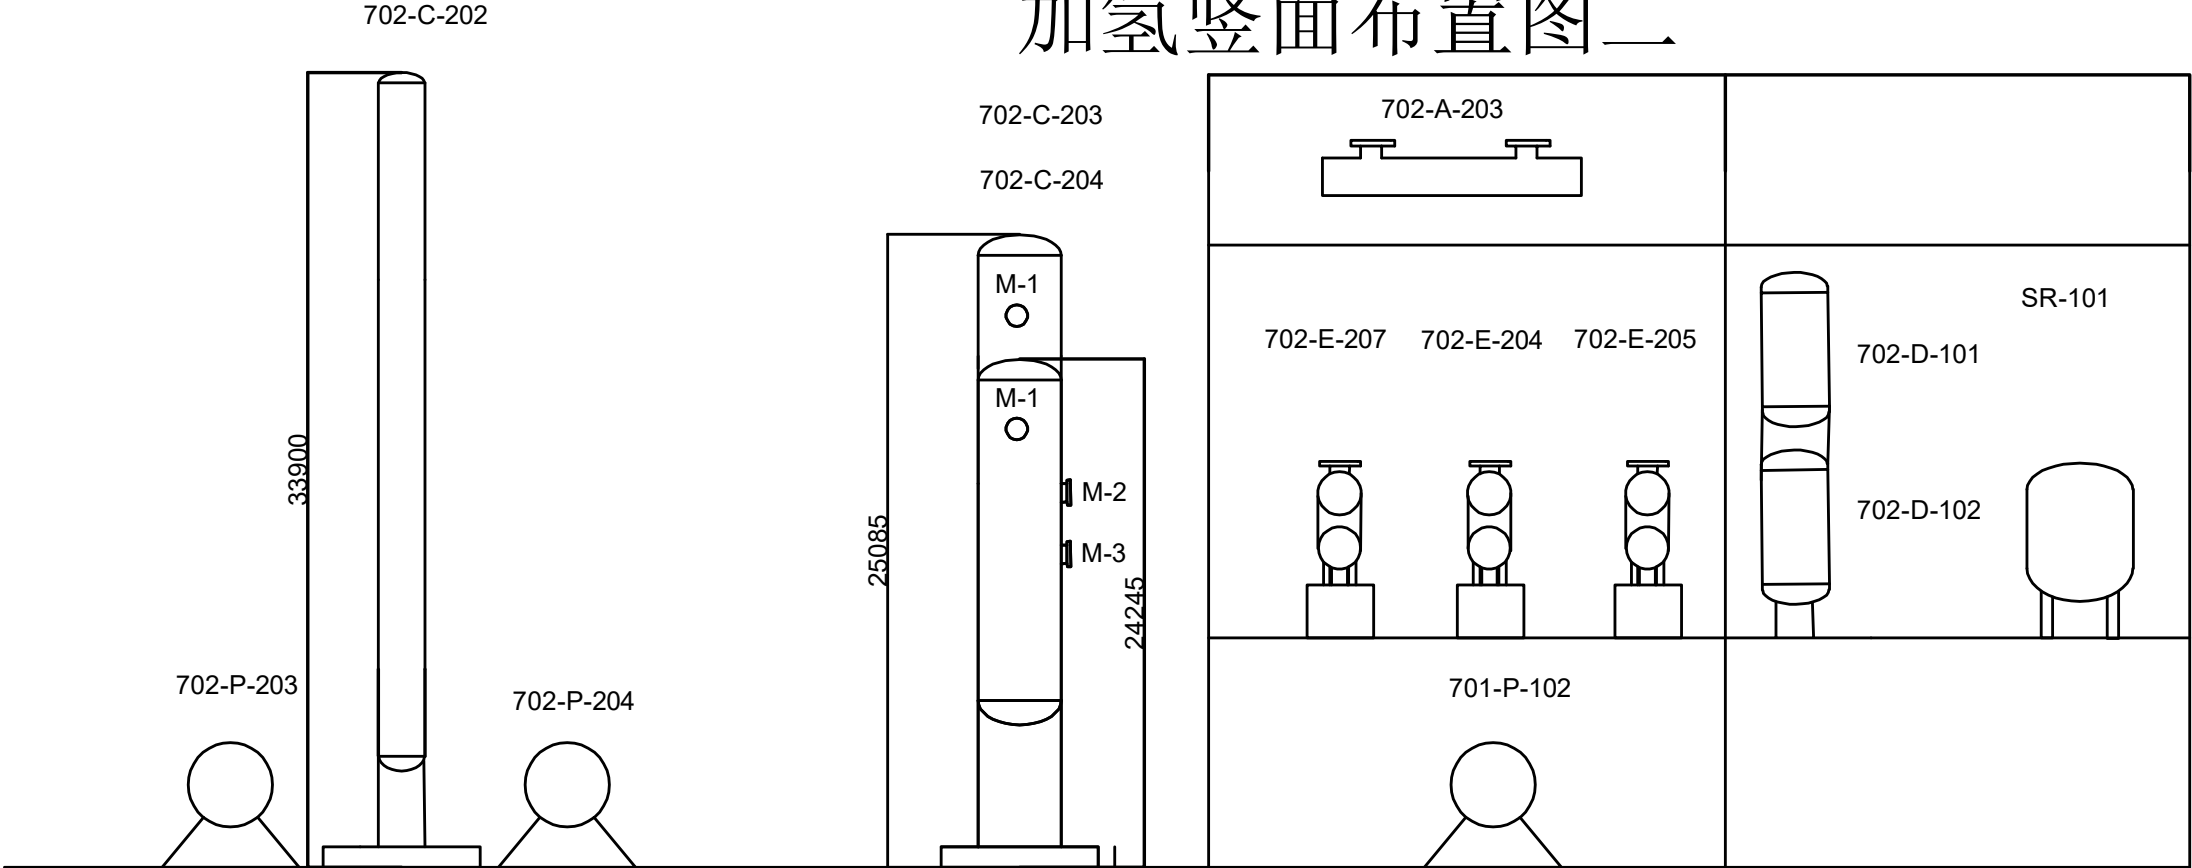

加氢竖面布置图三

