




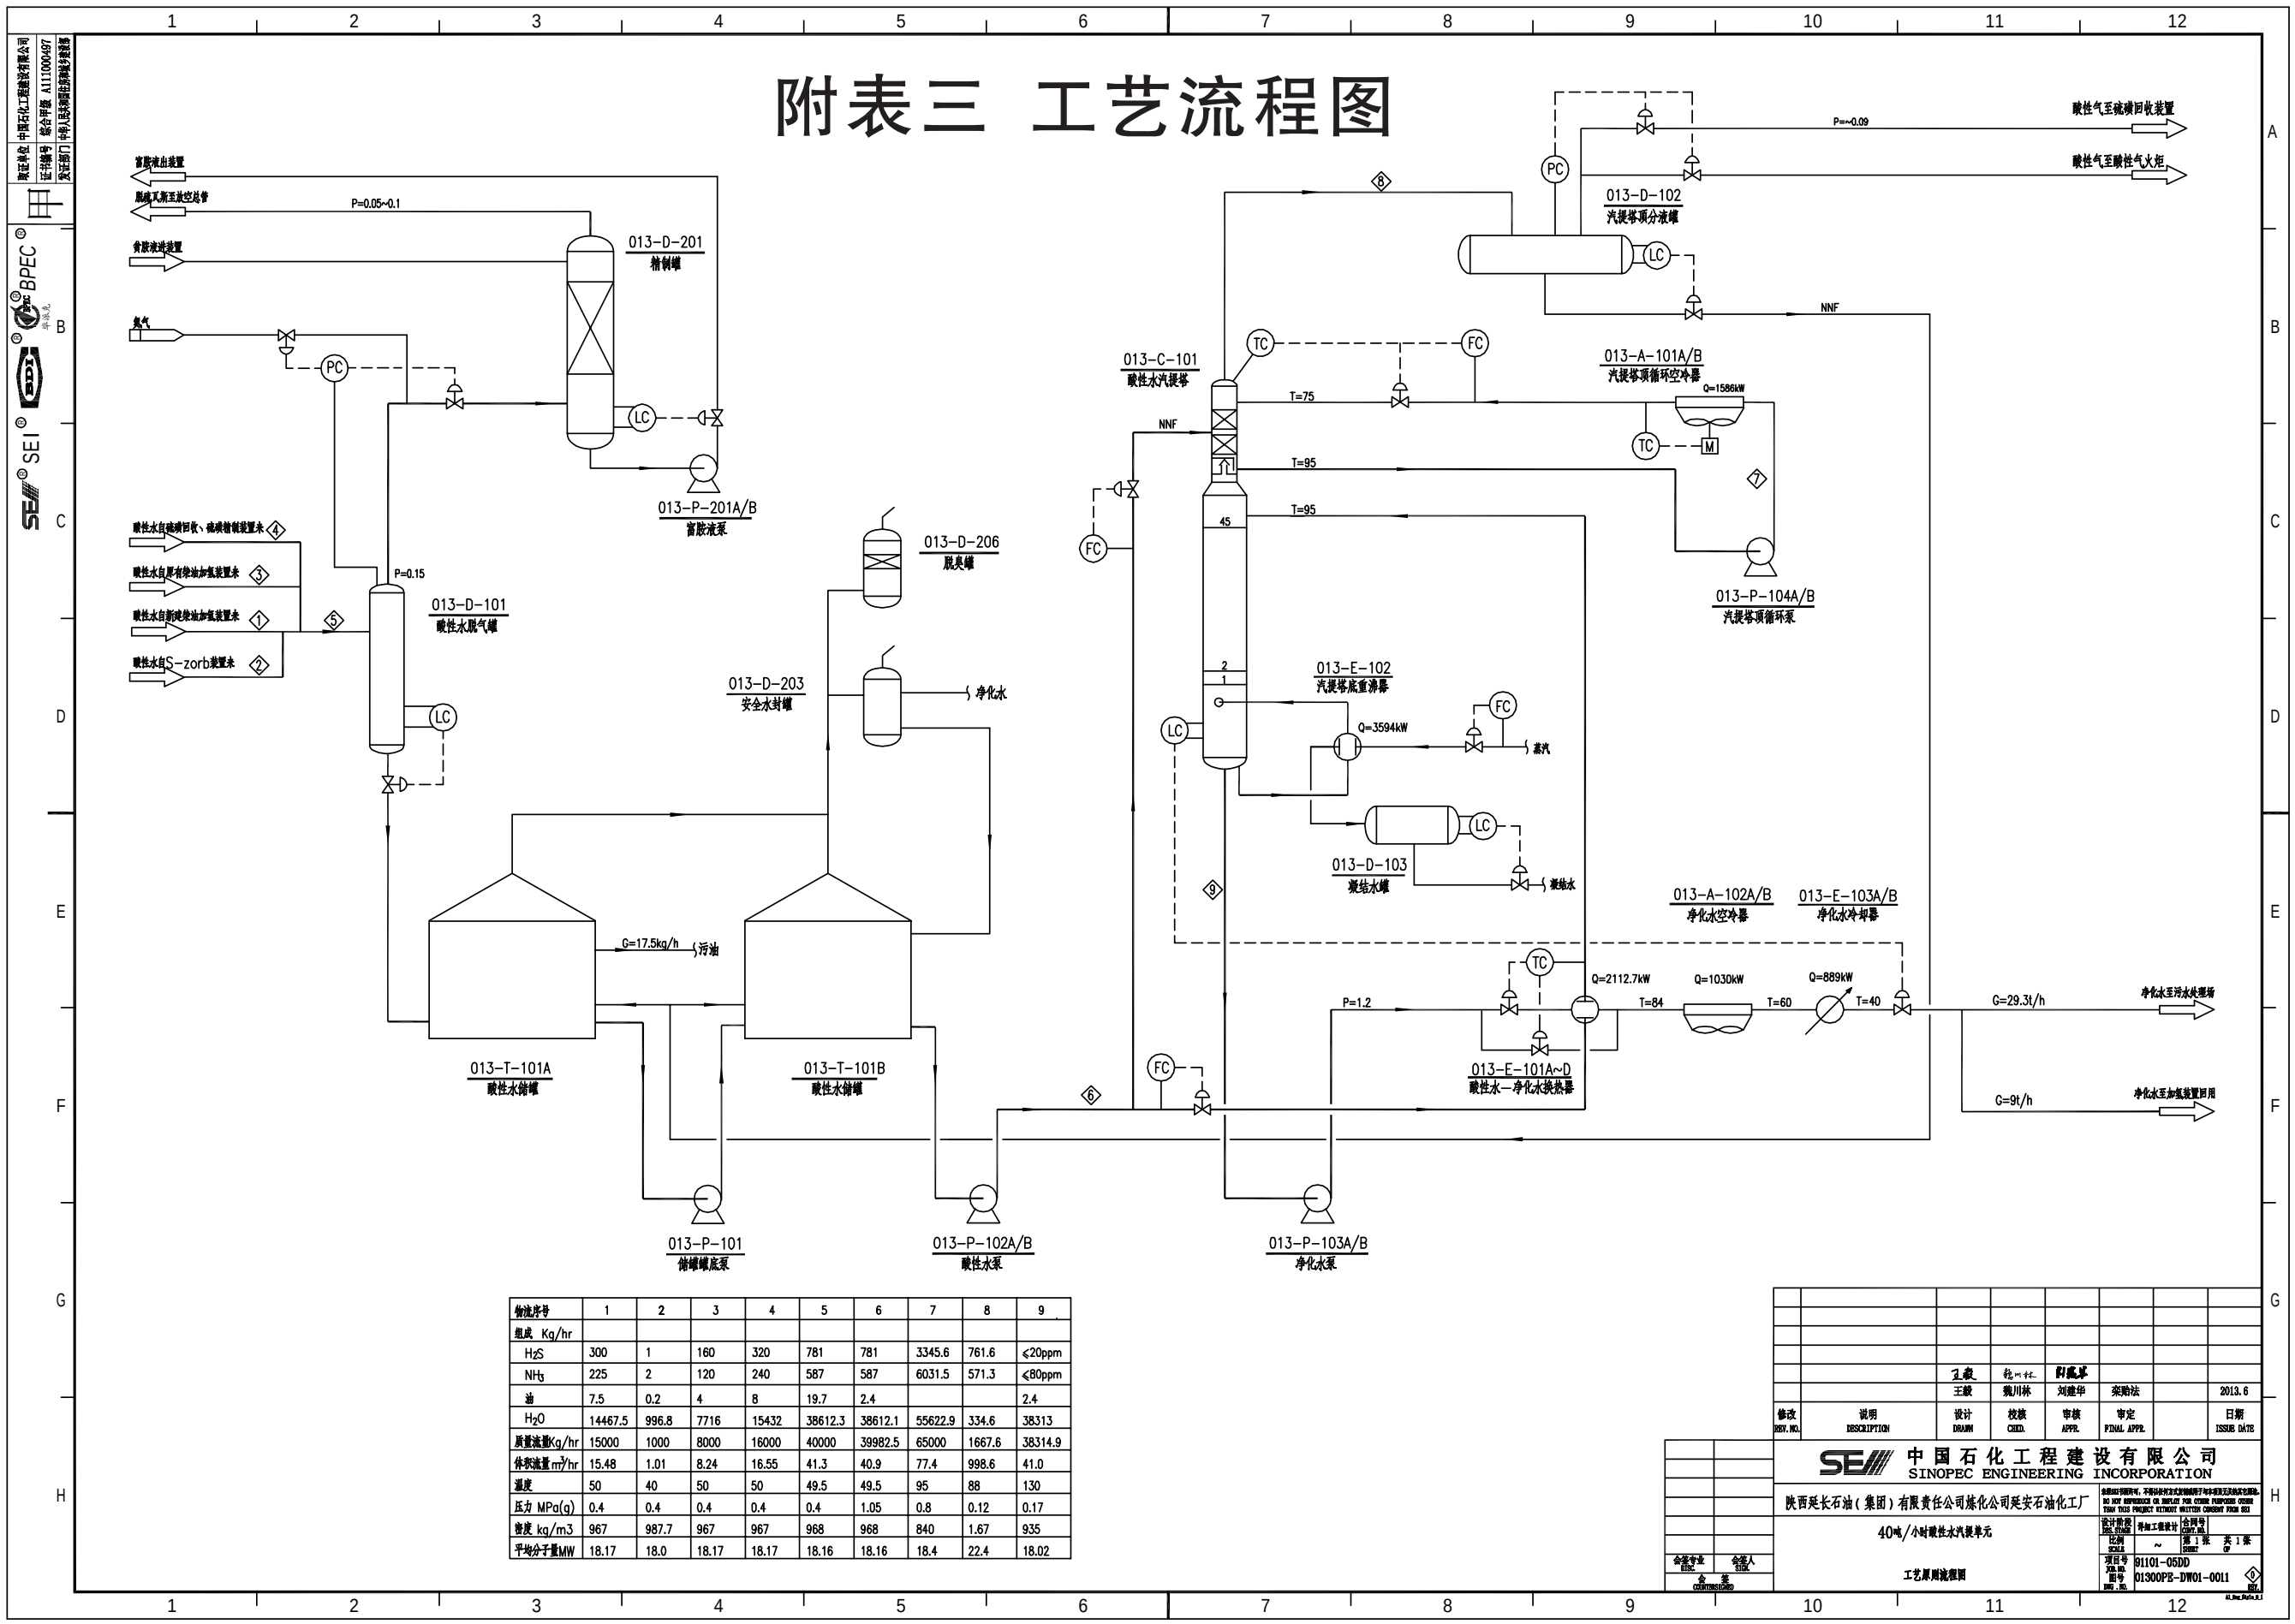


附件五 设备竖面布置图

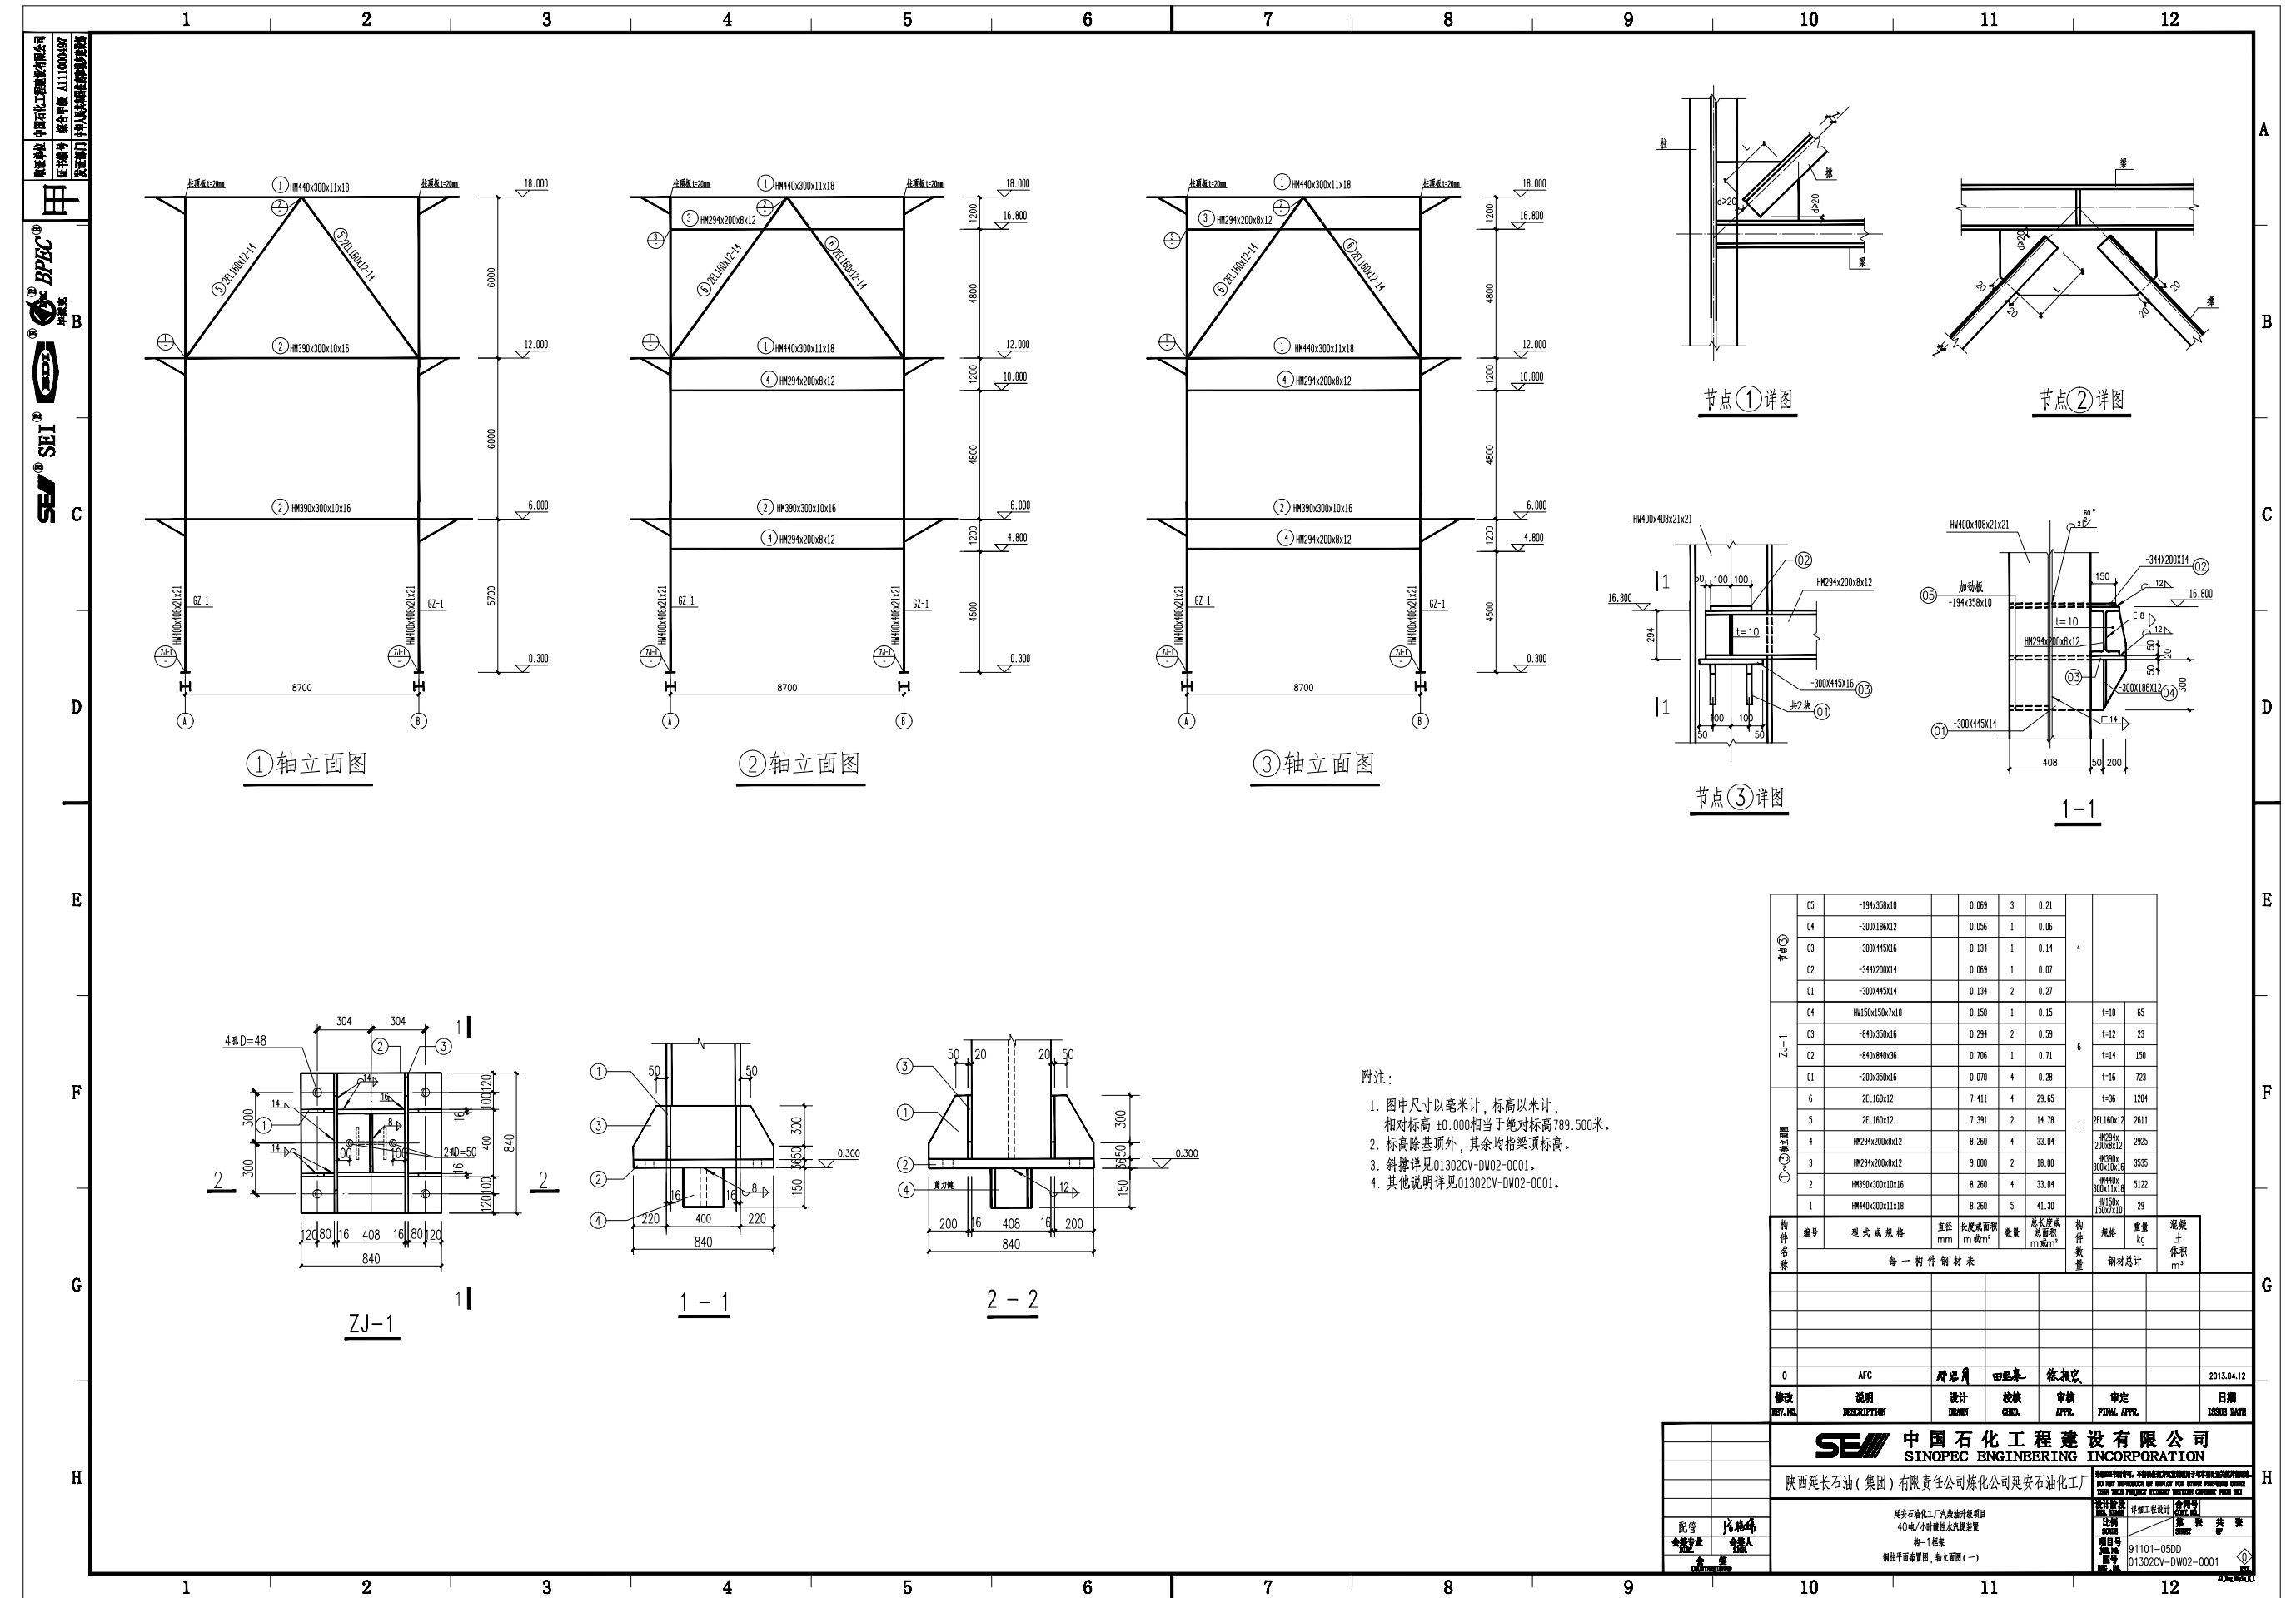

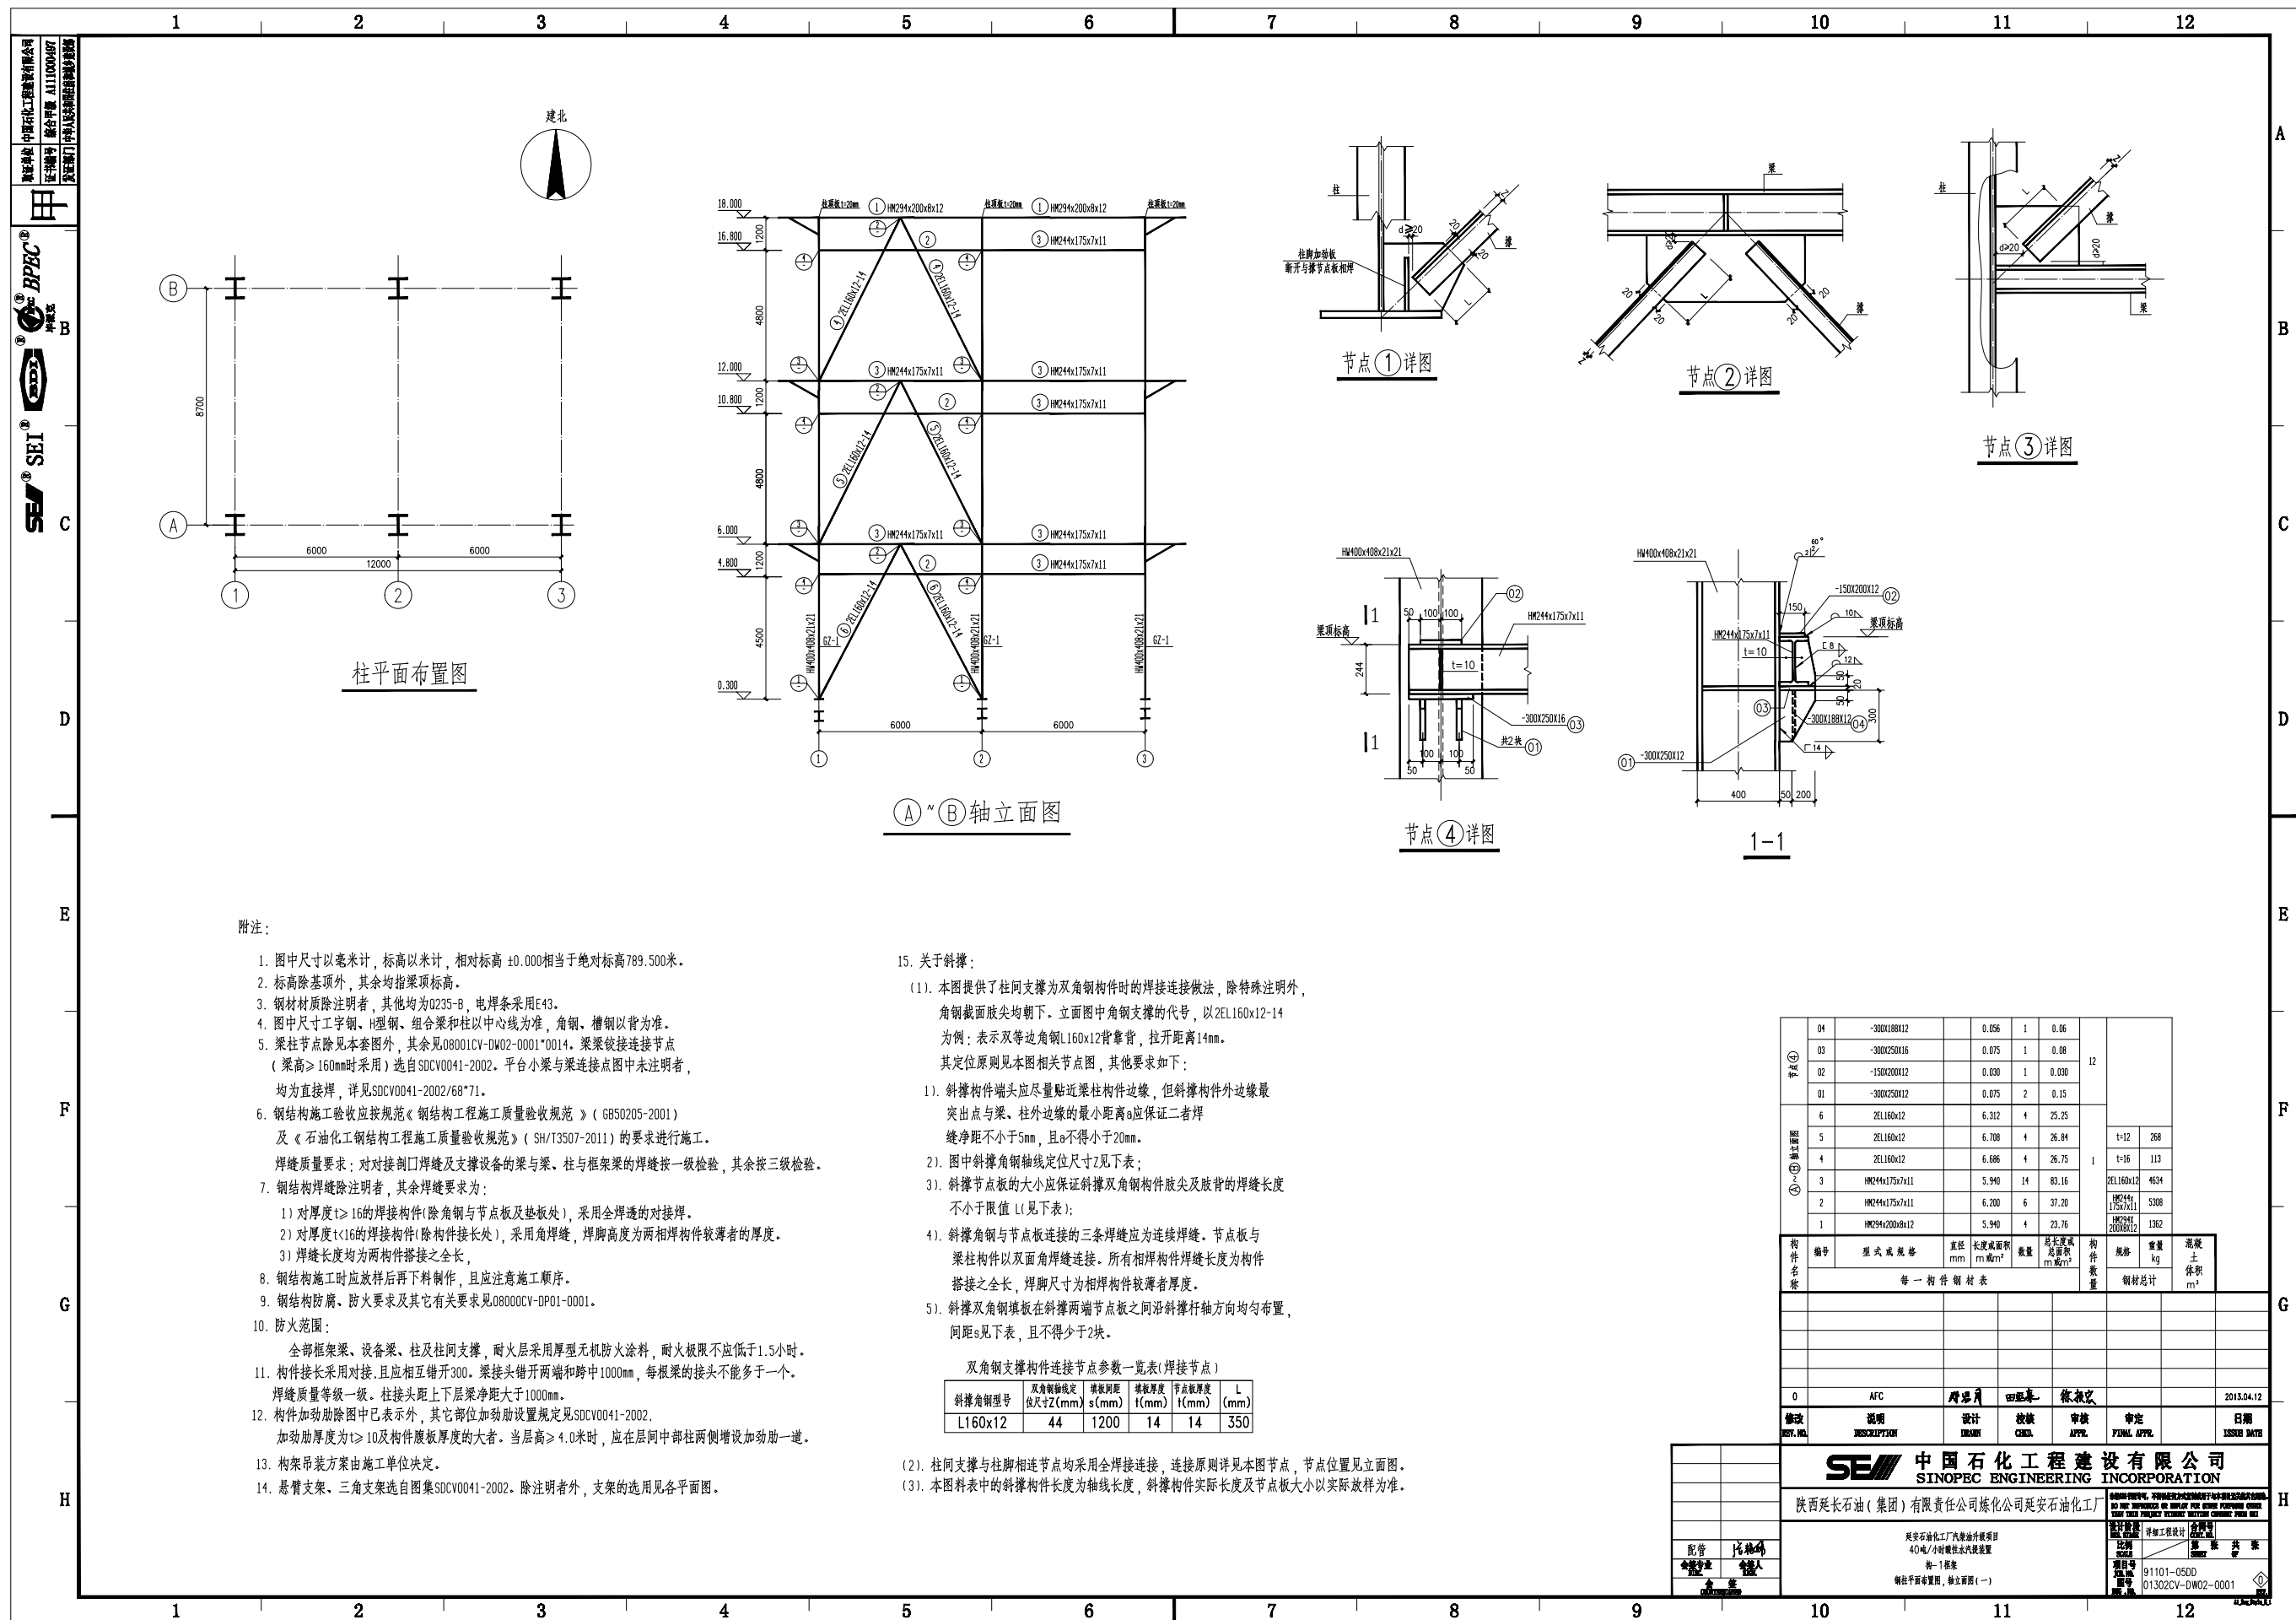

酸性水汽提塔（C-101）结构简图

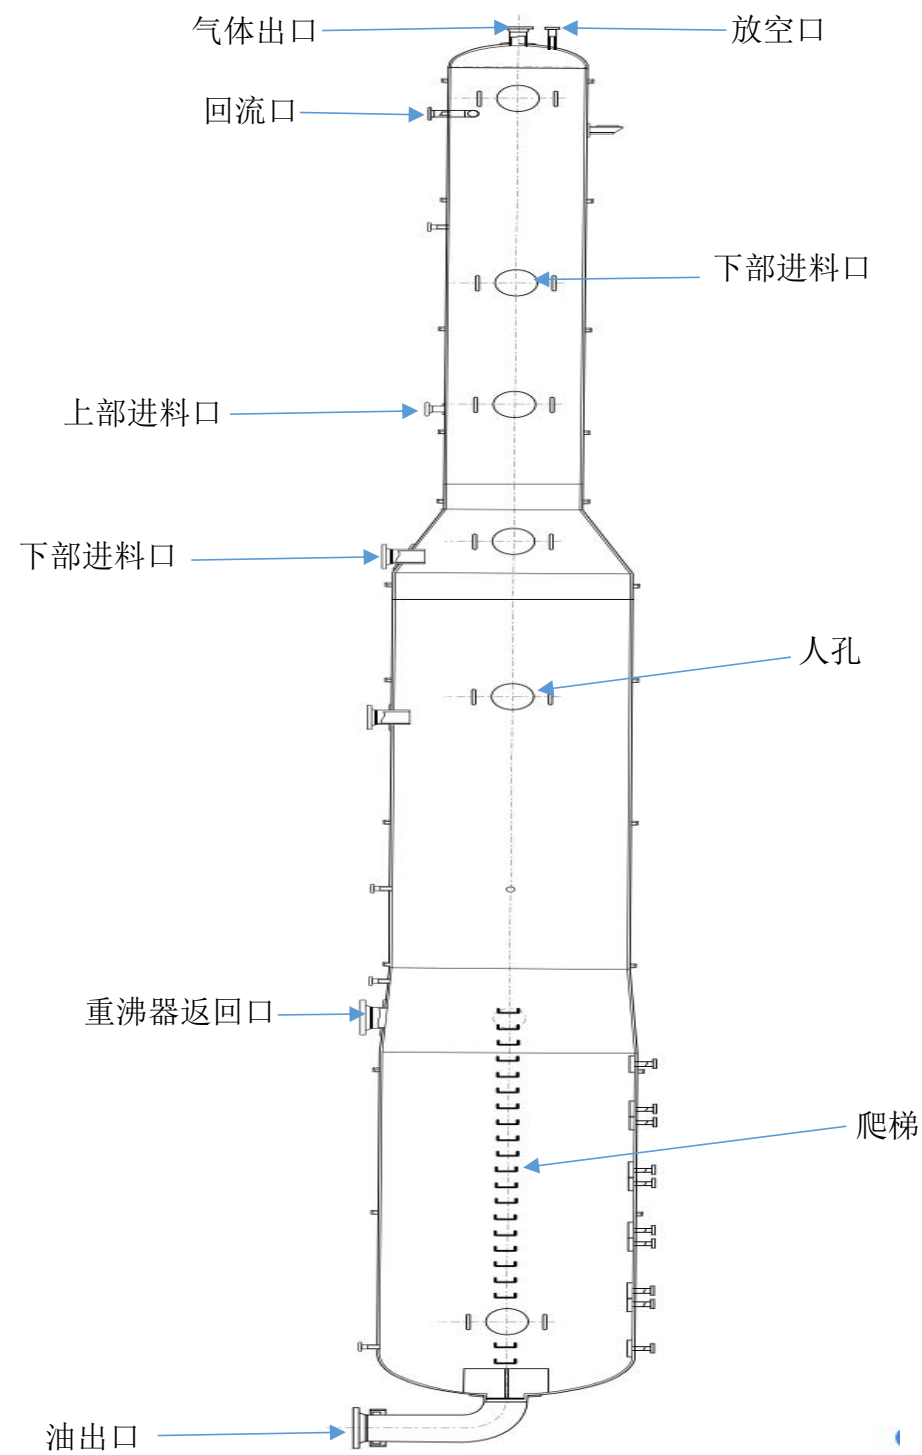

制图:	宋晓路
审核:	李宝强

附件七 可燃/有毒气体检测报警器汇总表

车间	位号	装置	可燃/有毒气体检测报警器					
			检测物质	型号/参数	安装位置	限值设定（高报和高高报或者低报和最低报）	运行情况/ 检测情况	备注
联合三车间	013-AI1101	酸性水汽提	可燃气体	KS-3	D-204 东南侧	高报：25%LEL;高高报：50%LEL	正常投用	
联合三车间	013-AI1102	酸性水汽提	可燃气体	KS-3	P-103A/B 东南侧	高报：25%LEL;高高报：50%LEL	正常投用	
联合三车间	013-AI1103	酸性水汽提	可燃气体	KS-3	I-101B 东侧	高报：25%LEL;高高报：50%LEL	正常投用	
联合三车间	013-AI1104	酸性水汽提	可燃气体	KS-3	I-101A 东侧	高报：25%LEL;高高报：50%LEL	正常投用	
联合三车间	013-AI-1201	酸性水汽提	硫化氢	DS-100	C-101 南侧	高报：5mg/m³;高高报：10mg/m³	正常投用	
联合三车间	013-AI-1202	酸性水汽提	硫化氢	DS-100	P-104A/B 中间	高报：5mg/m³;高高报：10mg/m³	正常投用	
联合三车间	013-AI-1203	酸性水汽提	硫化氢	DS-100	P-102A/B 中间	高报：5mg/m³;高高报：10mg/m³	正常投用	
联合三车间	013-AI-1204	酸性水汽提	硫化氢	DS-100	P-101 东侧	高报：5mg/m³;高高报：10mg/m³	正常投用	
联合三车间	013-AI-1205	酸性水汽提	硫化氢	DS-100	I-101B 东侧	高报：5mg/m³;高高报：10mg/m³	正常投用	
联合三车间	013-AI-1206	酸性水汽提	硫化氢	DS-100	I-101A 西侧	高报：5mg/m³;高高报：10mg/m³	正常投用	
联合三车间	013-AI-1207	酸性水汽提	硫化氢	DS-100	D-207 下方	高报：5mg/m³;高高报：10mg/m³	正常投用	
联合三车间	013-AI-1208	酸性水汽提	硫化氢	DS-100	D-101 东侧	高报：5mg/m³;高高报：10mg/m³	正常投用	
联合三车间	013-AI-1209	酸性水汽提	硫化氢	DS-100	D-201 东侧	高报：5mg/m³;高高报：10mg/m³	正常投用	